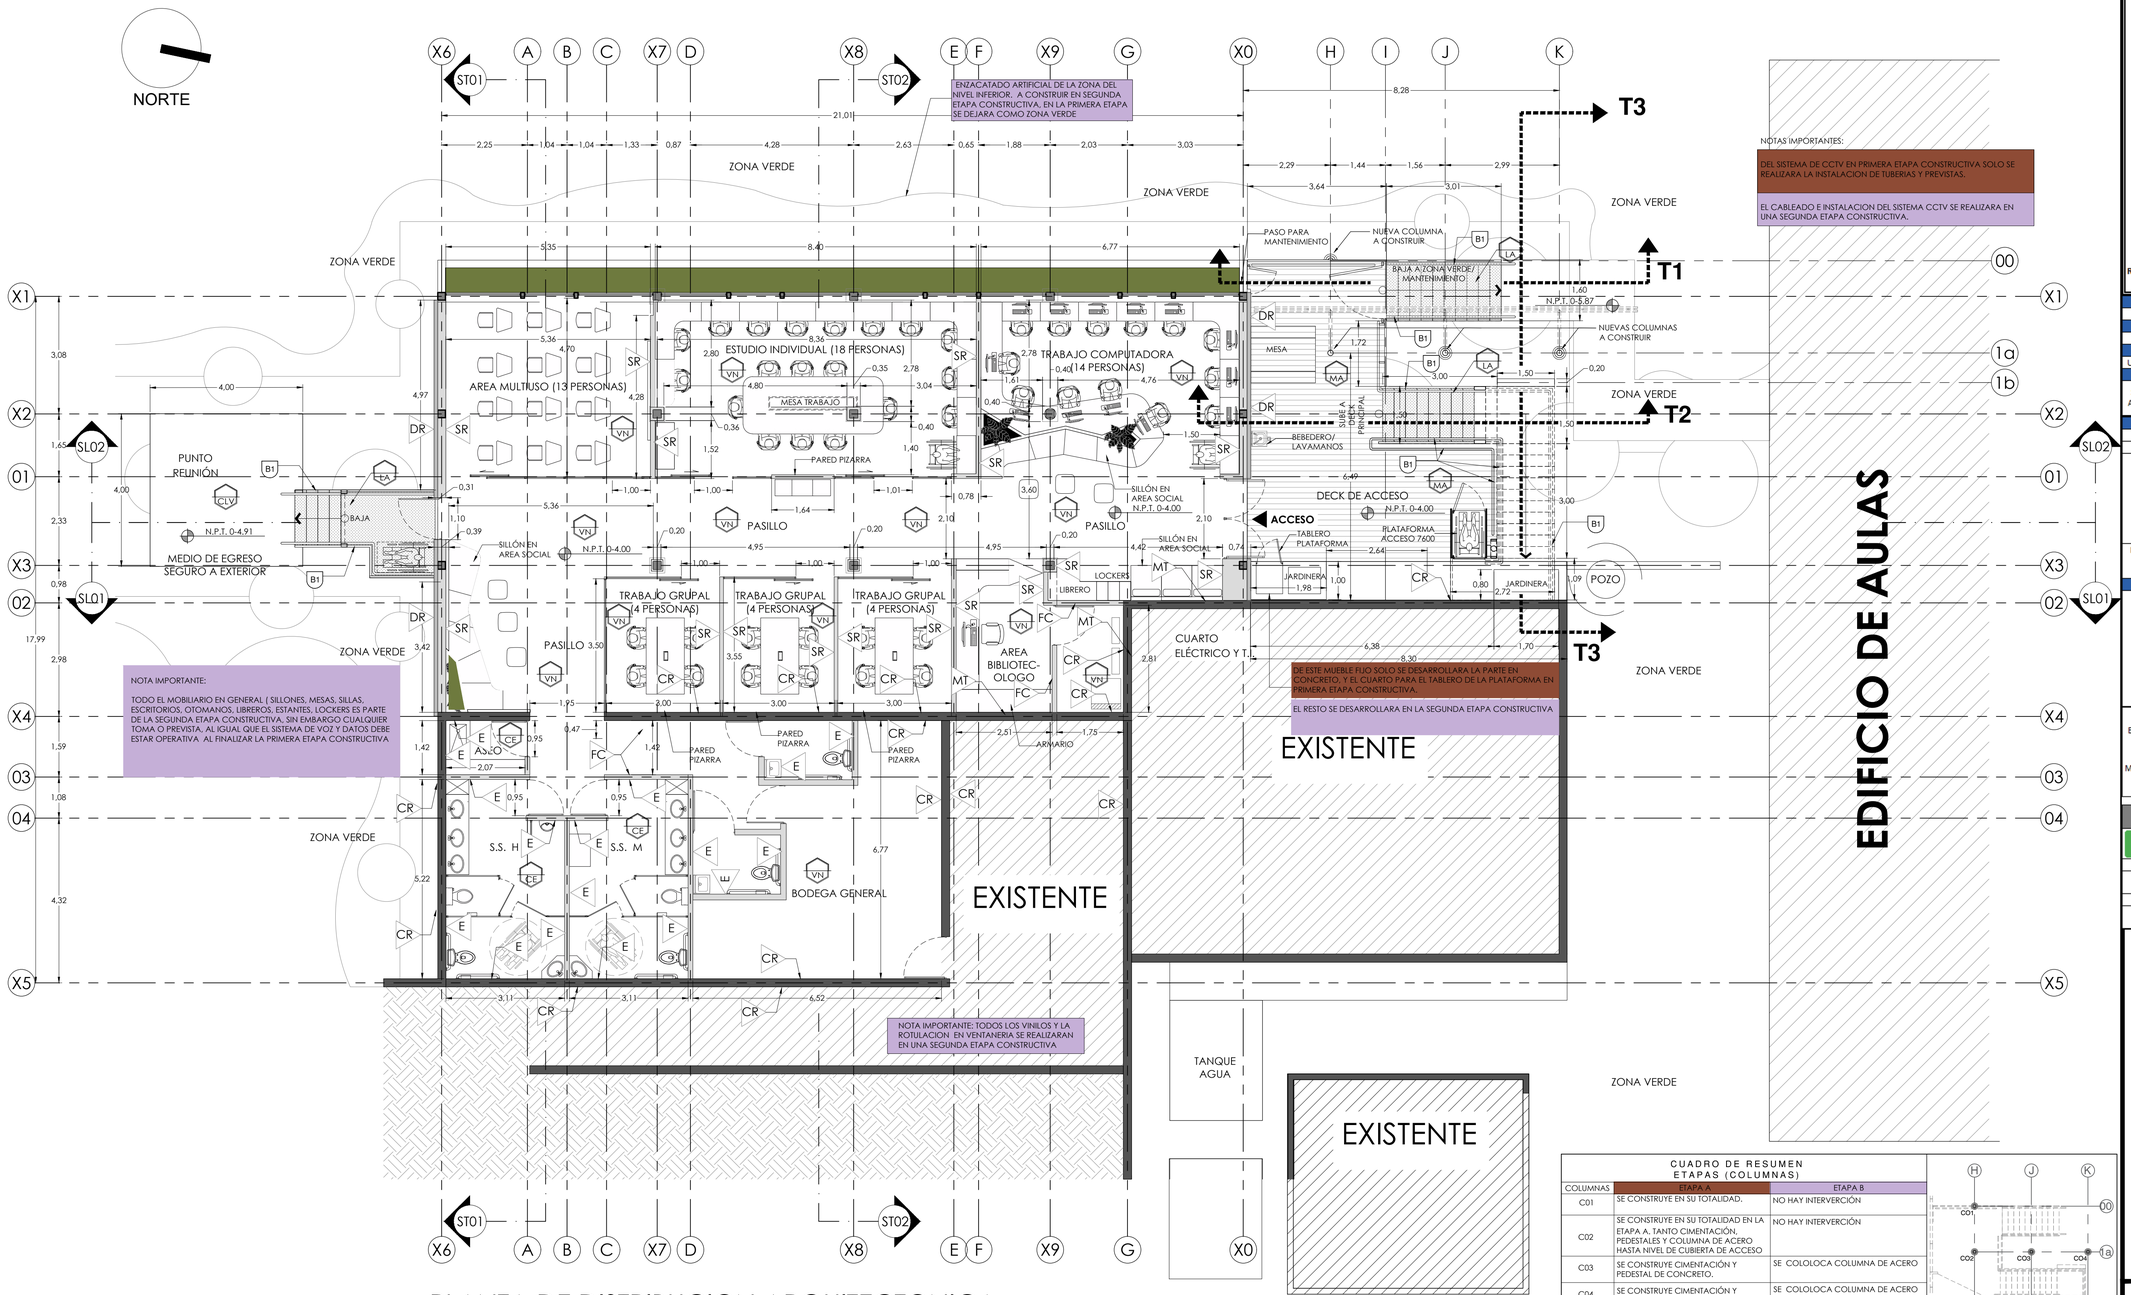

NOTA IMPORTANTE:

TODO EL MOBILIARIO EN GENERAL (SILLONES, MESAS, SILLAS, ESCRITORIOS, OTOMANOS, LIBREROS, ESTANTES, LOCKERS ES PARTE DE LA SEGUNDA ETAPA CONSTRUCTIVA, SIN EMBARGO CUALQUIER TOMA O PREVISTA, AL IGUAL QUE EL SISTEMA DE VOZ Y DATOS DEBE ESTAR OPERATIVA AL FINALIZAR LA PRIMERA ETAPA CONSTRUCTIVA

NOTAS IMPORTANTES:

DEL SISTEMA DE CCTV EN PRIMERA ETAPA CONSTRUCTIVA SOLO SE REALIZARA LA INSTALACION DE TUBERIAS Y PREVISTAS.

EL CABLEADO E INSTALACION DEL SISTEMA CCTV SE REALIZARA EN UNA SEGUNDA ETAPA CONSTRUCTIVA.

PLANTA DE DISTRIBUCION ARQUITECTONICA

ESCALA 1: 75

AREA DE INTERVENCIÓN: 336.60m2

CUADRO DE RESUMEN ETAPAS (COLUMNAS)

COLUMNAS	ETAPA A	ETAPA B
C01	SE CONSTRUYE EN SU TOTALIDAD.	NO HAY INTERVERCIÓN
C02	SE CONSTRUYE EN SU TOTALIDAD EN LA ETAPA A, TANTO CIMENTACIÓN, PEDESTALES Y COLUMNA DE ACERO HASTA NIVEL DE CUBIERTA DE ACCESO	NO HAY INTERVERCIÓN
C03	SE CONSTRUYE CIMENTACIÓN Y PEDESTAL DE CONCRETO.	SE COLOLOCA COLUMNA DE ACERO
C04	SE CONSTRUYE CIMENTACIÓN Y PEDESTAL DE CONCRETO.	SE COLOLOCA COLUMNA DE ACERO
C05	SE CONSTRUYE CIMENTACIÓN Y PEDESTAL DE CONCRETO.	SE COLOLOCA COLUMNA DE ACERO
C06	SE CONSTRUYE CIMENTACIÓN Y PEDESTAL DE CONCRETO.	SE COLOLOCA COLUMNA DE ACERO
C07	SE CONSTRUYE CIMENTACIÓN Y PEDESTAL DE CONCRETO.	SE COLOLOCA COLUMNA DE ACERO

NOTA IMPORTANTE:
LA CUBIERTA DE ACCESO SERA COLOCADA EN LA ETAPA B

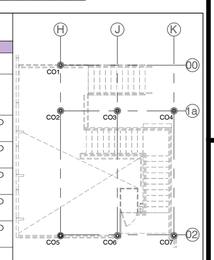

cfia
Colegio Federado de Ingenieros y de Arquitectos de Costa Rica

CONTRATO	OC 1065335
MONTO	¢ 375,545,804.00
FECHA VISADO CFIA	18/11/2022
CATASTRO	A-1733765-2014
ÁREA DE TASACIÓN (CFIA)	456 M2
REGISTRADO POR BITACORA	03027

ESTE SELLO TIENE UNA VIGENCIA DE UN AÑO, VENCE EL 18/11/2023 (vencimiento aplica sólo a planos constructivos)

SI NO HAY CONCORDANCIA ENTRE LA INFORMACIÓN DEL SELLO Y EL RESULTADO DE LA CONSULTA MEDIANTE EL CÓDIGO, EL SELLO ES NULO.

NOMBRE DEL PROYECTO	
Centro de Referencia Digital, Sede San Carlos	
CLASIFICACIÓN SEGÚN DECRETO 36550	
PROYECTOS NO CLASIFICADOS (REVISADO POR MS Y BOMBEROS)	
PROPIETARIO	CÉDULA
UNIVERSIDAD TÉCNICA NACIONAL	3-007-556085
DIRECCIÓN	UBICACIÓN
SEDE REGIONAL ECOCAMPUS, LA ABUNDANCIA, CIUDAD QUESADA.	PROVINCIA: ALAJUELA CANTÓN: SAN CARLOS DISTRITO: QUESADA
Elaboración de planos y documentos	
ESTUDIOS PRELIMINARES	A-8437 RAMIREZ ARAYA ISIDRO
ANTEPROYECTO	A-8437 RAMIREZ ARAYA ISIDRO
PLANOS Y ESPECIFICACIONES TÉCNICAS	A-8437 RAMIREZ ARAYA ISIDRO
	IC-0958, II-0958 CAÑAS RUIZ RAFAEL EDUARDO
	IE-15276 CASTRO HERRERA MARCO ANDREY
	IM-8408 OCAMPO RODRIGUEZ KARINA MARIA
ESTIMACIÓN GLOBAL DE COSTOS	A-8437 RAMIREZ ARAYA ISIDRO
	IC-10225 BRENES ECHEVERRIA JOSE JAVIER
CONTROL DE LA EJECUCIÓN DEL PROYECTO	
INSPECCION	A-8437 RAMIREZ ARAYA ISIDRO Fecha: 17/11/2022
	IC-10225 BRENES ECHEVERRIA JOSE JAVIER
	IC-0958, II-0958 CAÑAS RUIZ RAFAEL EDUARDO
	IM-8408 OCAMPO RODRIGUEZ KARINA MARIA
	IE-15276 CASTRO HERRERA MARCO ANDREY

ATENCIÓN MUNICIPALIDAD

Este proyecto no cuenta con profesional responsable de ejecución de obra

No puede tramitarse la SOLICITUD DE MEDIDORES, ni el PERMISO MUNICIPAL hasta que se complete la información bajo esta leyenda y se cuente con el sello del Colegio Federado de Ingenieros y Arquitectos de Costa Rica

RESULTADO DE LA REVISION INSTITUCIONAL	
✓ INFORME DE CUMPLIMIENTO SIN OBSERVACIONES	
Bomberos	
SUBSANACIÓN ACEPTADA	ING.ISABEL MARÍN ROJAS 19 Jan 2023
Ministerio de Salud	
SUBSANACIÓN ACEPTADA	Claudia Puentes Mojica 25 Jan 2023

CONTENIDO:

PLT ARQUITECTONICA NIVEL CENTRO REFERENCIA DIGITAL

CENTRO DE REFERENCIA DIGITAL

SEDE REGIONAL SAN CARLOS, LA ABUNDANCIA, SAN CARLOS, ALAJUELA

Universidad Técnica Nacional

nortesur arquitectos
San José: tel. (506) 2234-6660 / Fax: (506) 2234-2829
San Carlos: tel. (506) 2460 8308 / Fax: (506) 2461 1234
info@nortesurarquitectos.com
www.nortesurarquitectos.com

REV.	ARQ	REVISO.	FECHA.	MODIFICACION.

INFORMACION DE REGISTRO PUBLICO:
PROPIETARIO: UNIVERSIDAD TÉCNICA NACIONAL
CÉDULA JURIDICA: 3-007-556085
CATASTRO: A-1733765-2014
FOLIO REAL: 082-084 TOMO 18610

FECHA:	CONSECUTIVO
MAYO 2022	A 03a