PLANO AS BUILT
JUNIO 2020

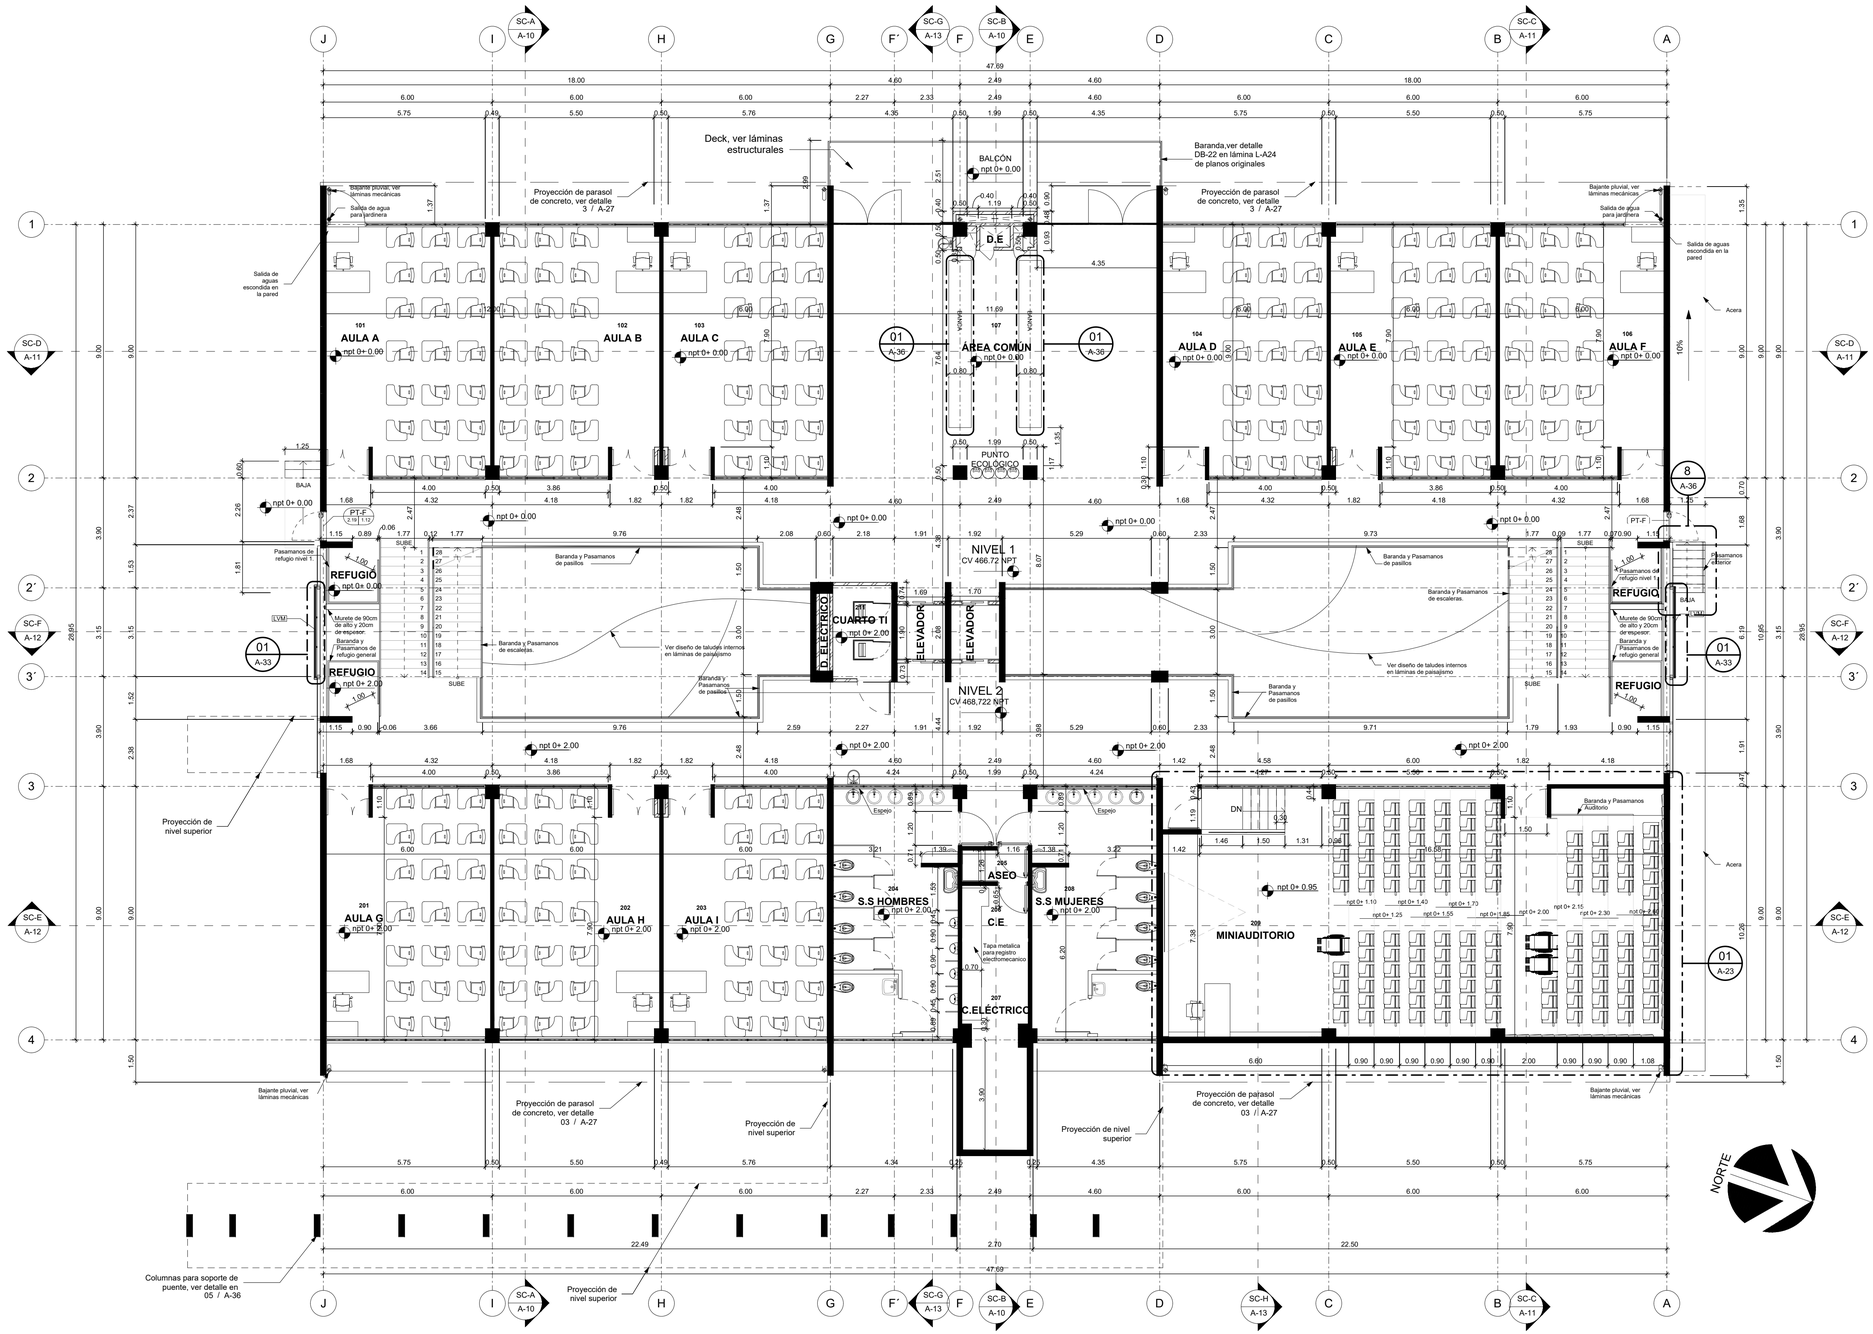

1 PLANTA DE DISTRIBUCIÓN ARQUITECTÓNICA - NIVEL 1 Y NIVEL 2
1 : 100

CONTENIDO:

PLANTA ARQUITECTÓNICA DIMENSIONAMIENTO NIVEL 1 - NIVEL 2

EDIFICIO DE AULAS UTN SEDE SAN CARLOS

LA ABUNDANCIA , QUESADA, SAN CARLOS

Universidad Técnica Nacional

nortesur arquitectos
San José: tel. (506) 2234-6660 / Fax: (506) 2234-2829
San Carlos: tel. (506) 2460 8308 / Fax: (506) 2461 1234
info@nortesurarquitectos.com
www.nortesurarquitectos.com

REV:	ARQ:	REVISO:	FECHA:	MODIFICACIÓN:

INFORMACIÓN DEL REGISTRO PÚBLICO:
PROPIETARIO: UNIVERSIDAD TÉCNICA NACIONAL
CÉDULA: 3-007-556085

CATASTRO: A-1733765-2014
FOLIO REAL: 082-084 TOMO: 18610

FECHA: AGOSTO 2018

CONSECUTIVO: A-04 / A-37